


[3] Project Architecture

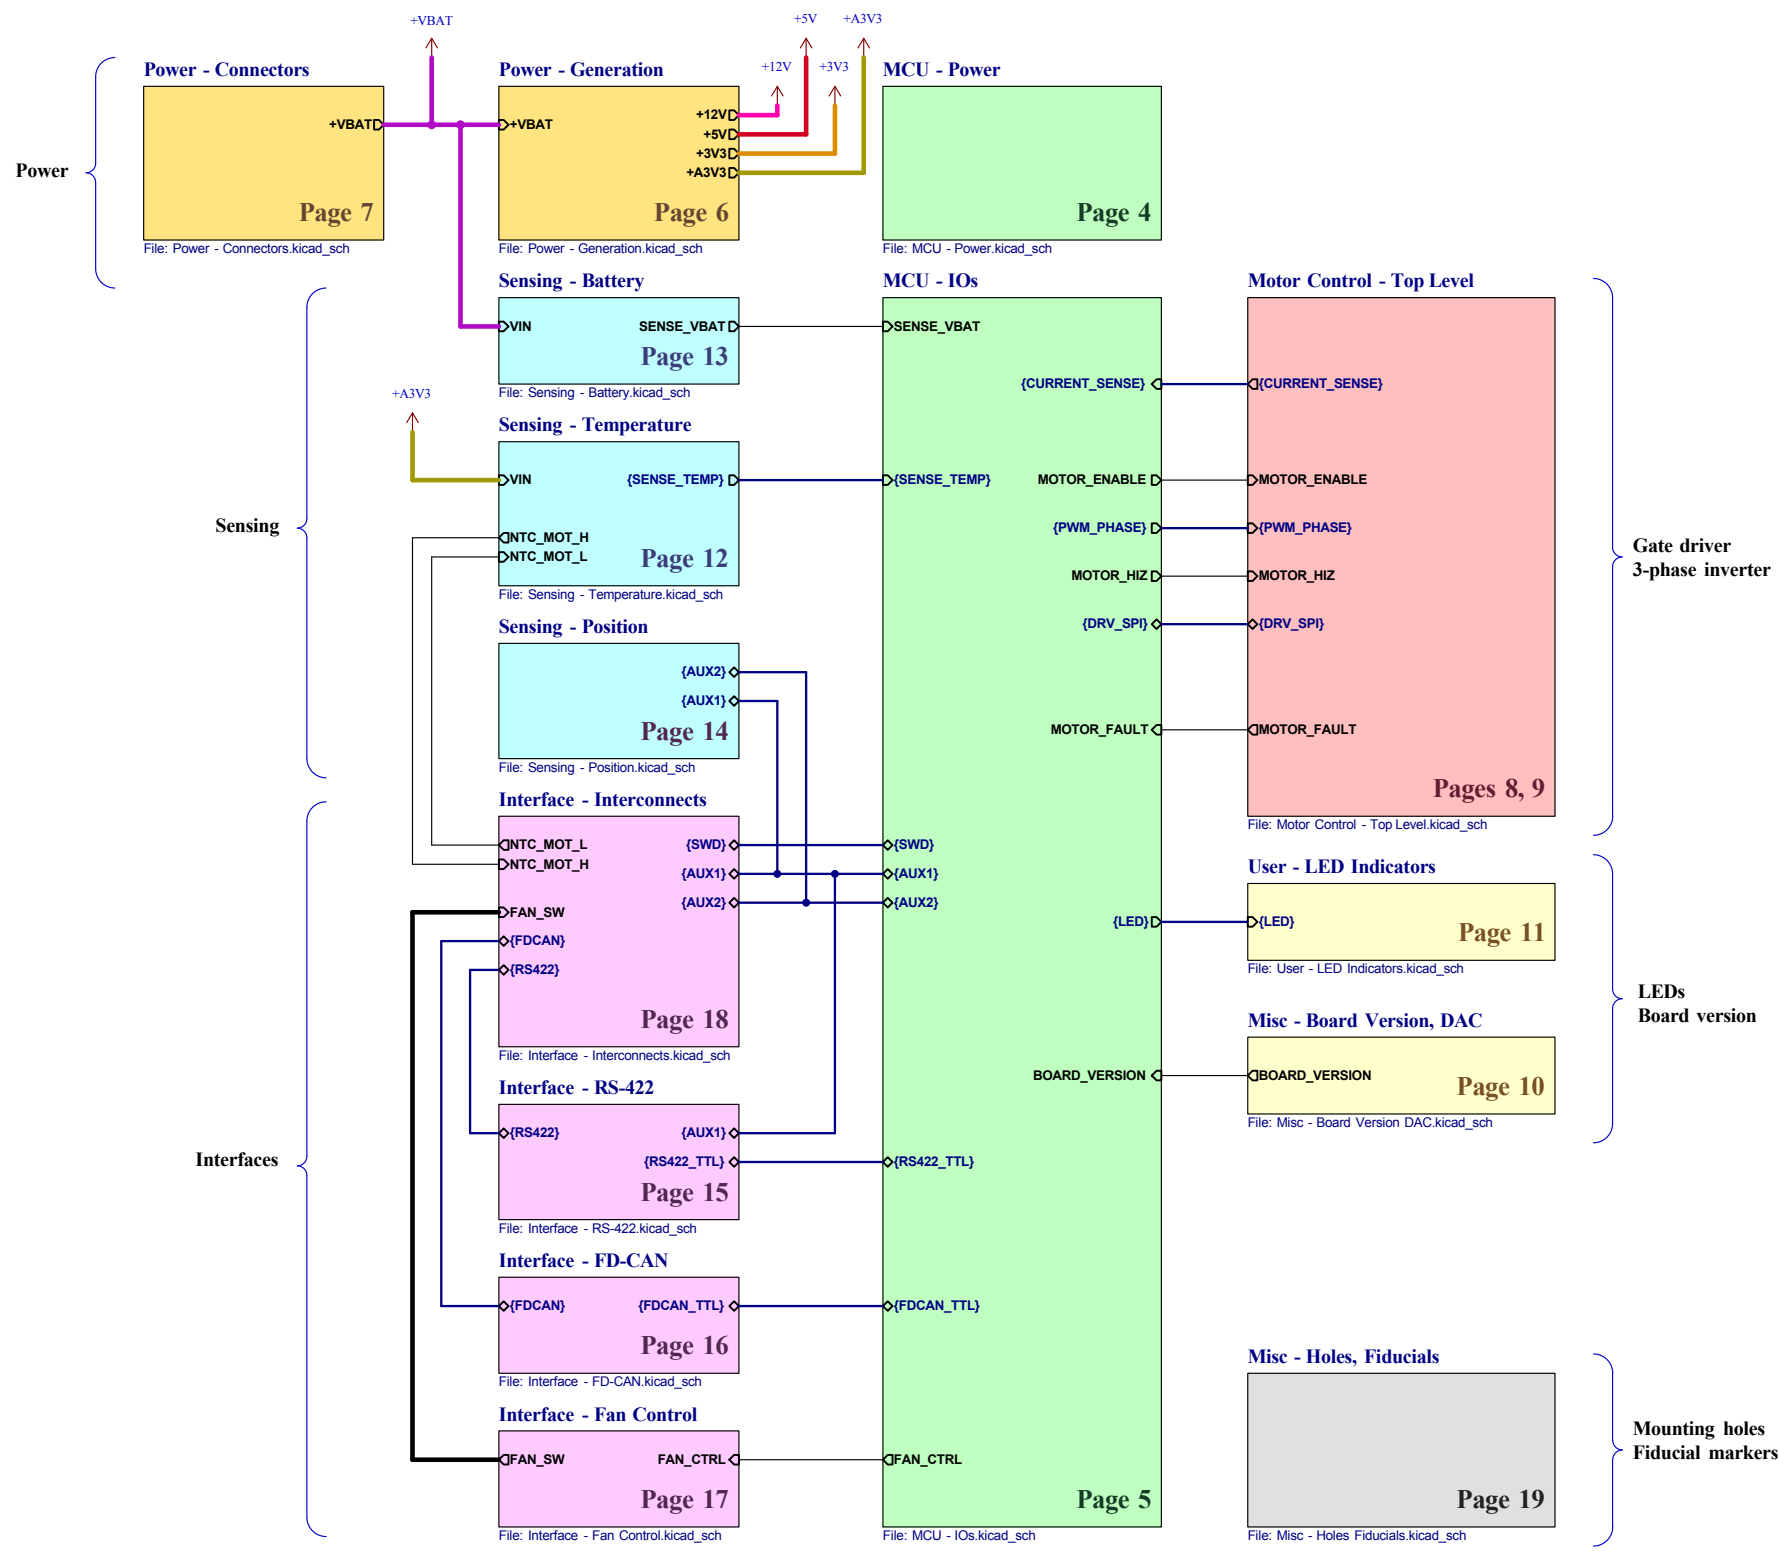

Comments:	Company:		Variant:	Git Hash:
	EPFL Xplore Research			5b68472
	Board Name:		Project Name:	
Sheet Title:	File Name:	Designer:	Date:	Revision:
Project Architecture	Project Architecture.kicad_sch	Vincent Nguyen	2023-12-22	1.1.1+ (Unreleased)
Sheet Path:	Reviewer:		Size:	Sheet:
/Project Architecture/			A3	3 of 21